


ПЕРЕПЛАНИРОВКА, ВАРИАНТ 2 / REPLANNING, VARIANT 2

М 1:50

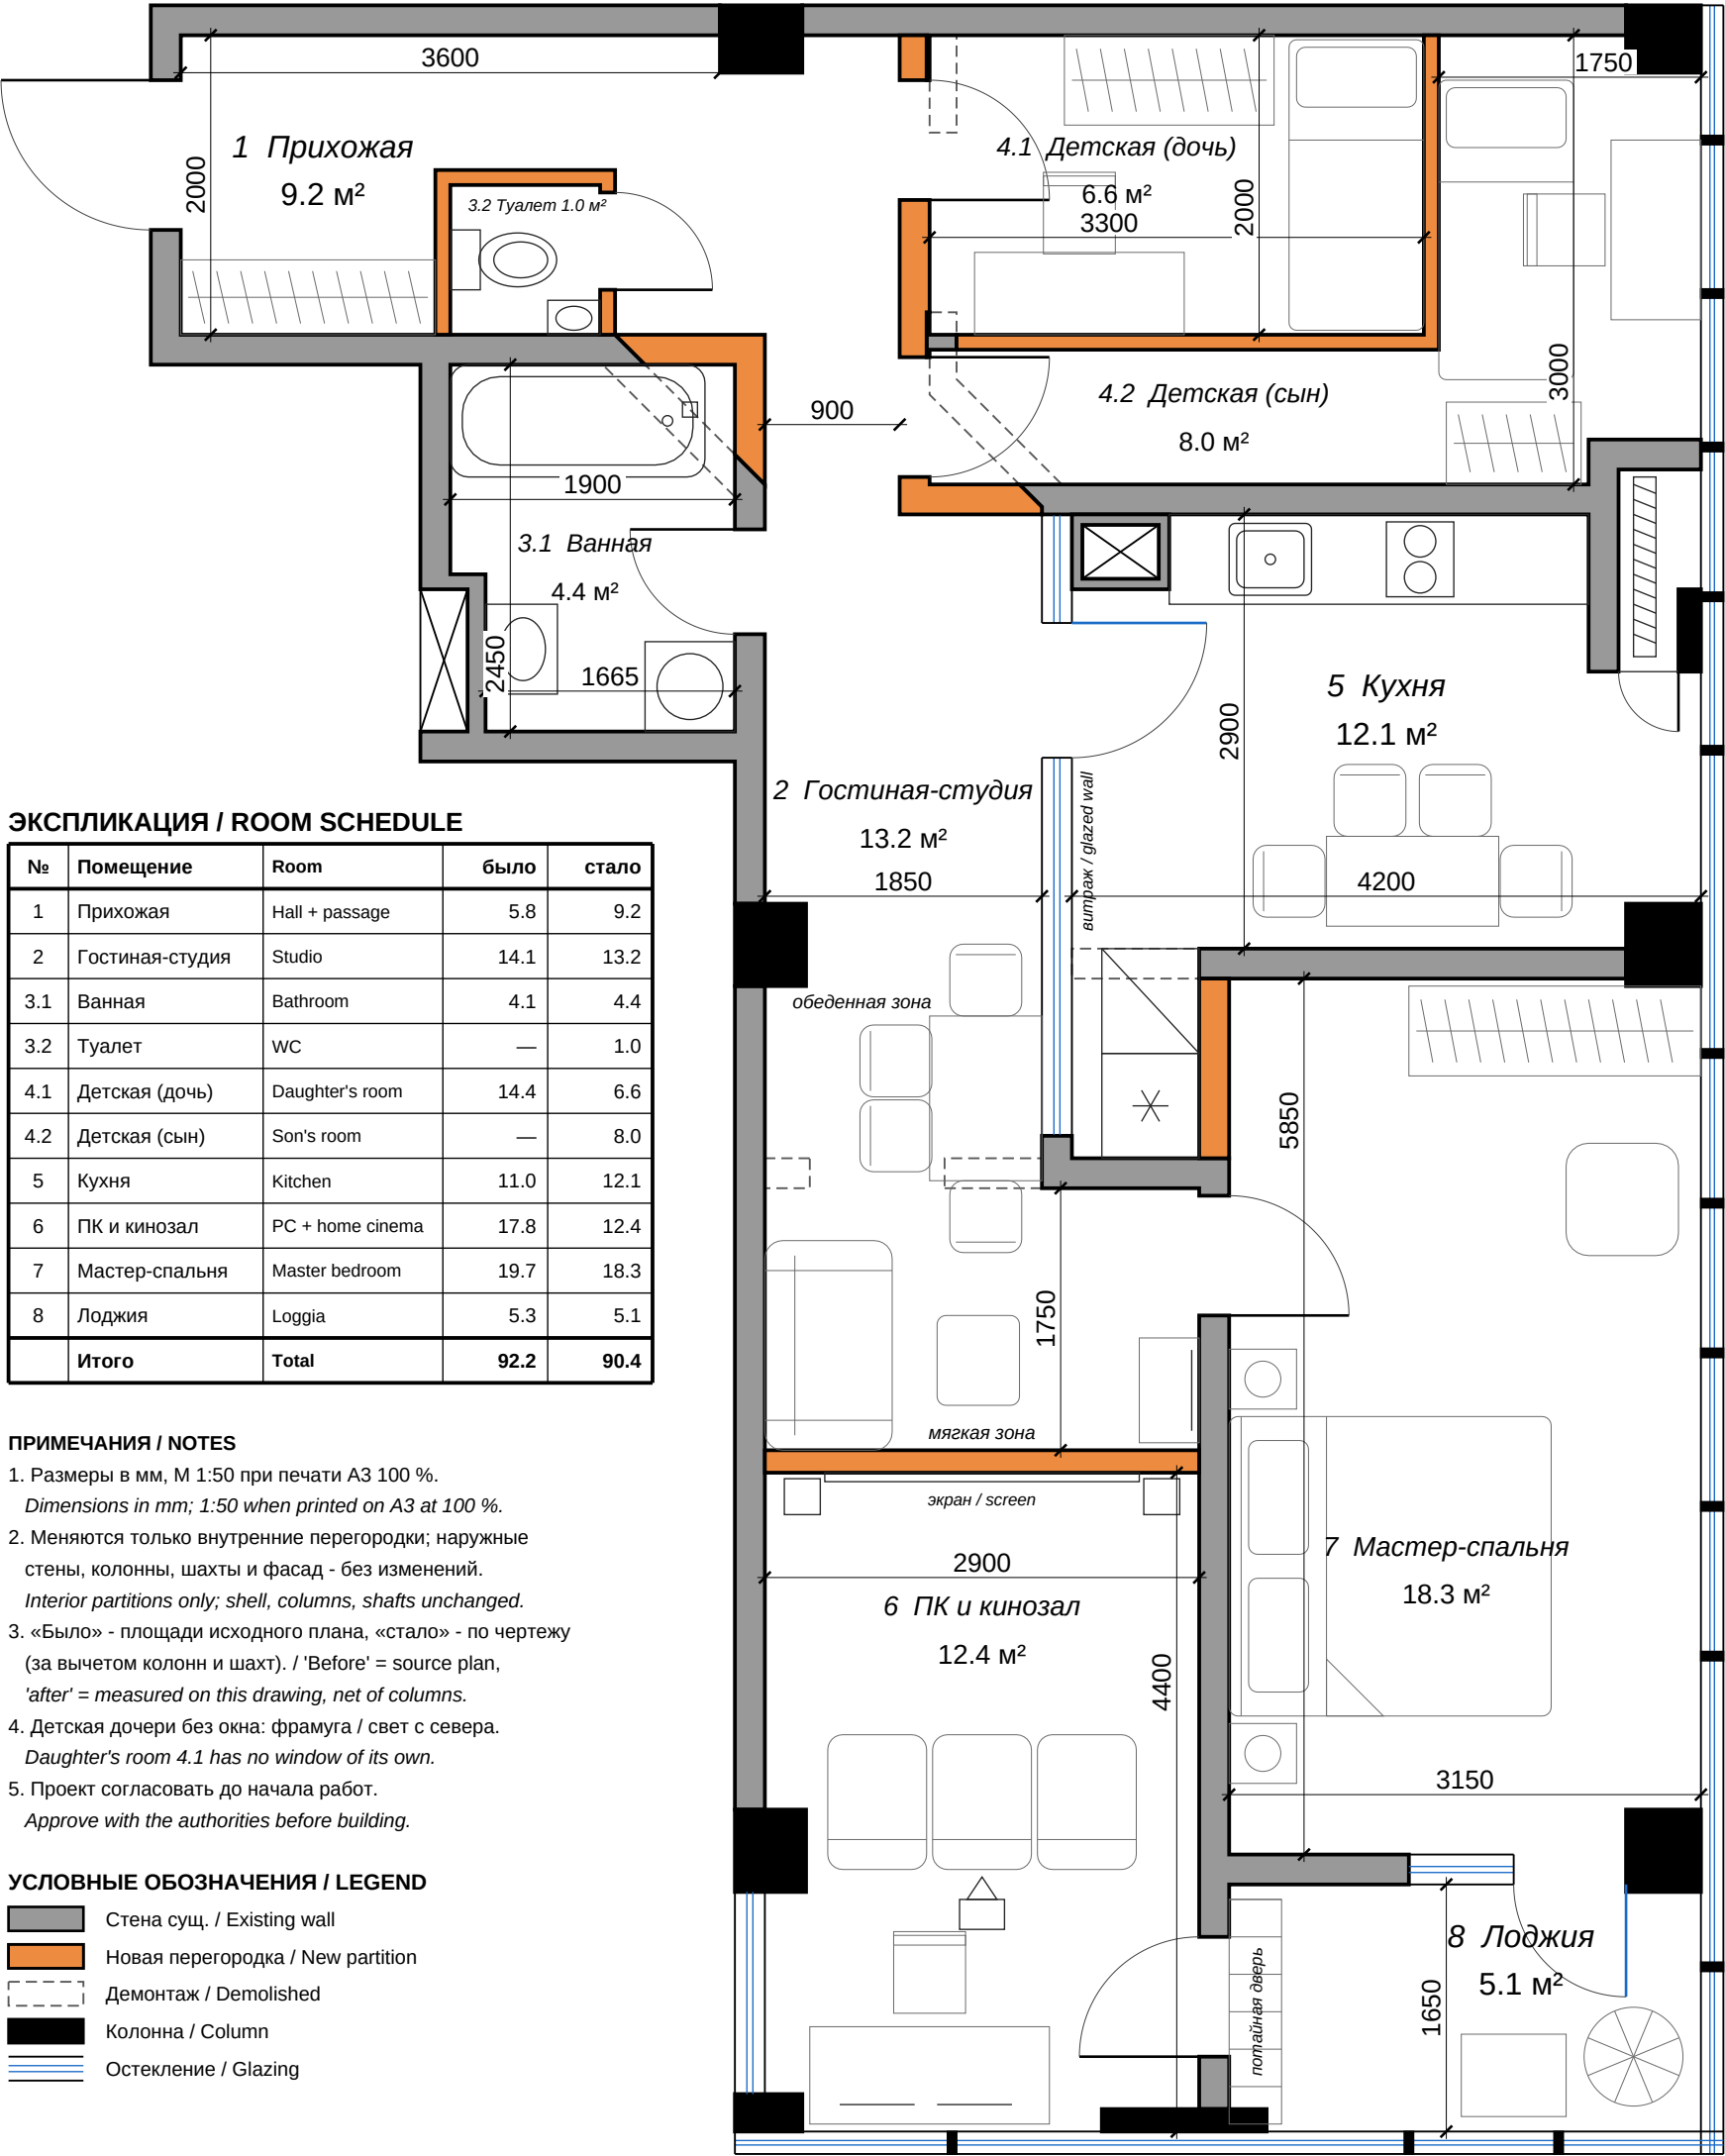

ЭКСПЛИКАЦИЯ / ROOM SCHEDULE

№	Помещение	Room	было	стало
1	Прихожая	Hall + passage	5.8	9.2
2	Гостиная-студия	Studio	14.1	13.2
3.1	Ванная	Bathroom	4.1	4.4
3.2	Туалет	WC	—	1.0
4.1	Детская (дочь)	Daughter's room	14.4	6.6
4.2	Детская (сын)	Son's room	—	8.0
5	Кухня	Kitchen	11.0	12.1
6	ПК и кинозал	PC + home cinema	17.8	12.4
7	Мастер-спальня	Master bedroom	19.7	18.3
8	Лоджия	Loggia	5.3	5.1
Итого		Total	92.2	90.4

ПРИМЕЧАНИЯ / NOTES

1. Размеры в мм, М 1:50 при печати А3 100 %.
Dimensions in mm; 1:50 when printed on A3 at 100 %.
2. Меняются только внутренние перегородки; наружные стены, колонны, шахты и фасад - без изменений.
Interior partitions only; shell, columns, shafts unchanged.
3. «Было» - площади исходного плана, «стало» - по чертежу (за вычетом колонн и шахт). / 'Before' = source plan, 'after' = measured on this drawing, net of columns.
4. Детская дочери без окна: фрамуга / свет с севера.
Daughter's room 4.1 has no window of its own.
5. Проект согласовать до начала работ.
Approve with the authorities before building.

УСЛОВНЫЕ ОБОЗНАЧЕНИЯ / LEGEND

- Стена сущ. / Existing wall
- Новая перегородка / New partition
- Демонтаж / Demolished
- Колонна / Column
- Остекление / Glazing

Масштабная линейка / Scale bar 1:50 (м / m)



План квартиры - вариант перепланировки 2

Apartment floor plan - replanning proposal, variant 2

Общая площадь / Total area (по чертежу / measured):
90.4 м² (в т.ч. лоджия / incl. loggia 5.1 м²)

Размеры в мм / Dimensions in mm
Основа / Base: output/flat-plan_1-50_A3.pdf

Масштаб / Scale
1:50

Формат / Size
A3

Лист / Sheet
3

Дата / Date
27.09.2026