


КВАРТИРАНИ ҚАЙТА РЕЖАЛАШТИРИШ РЕЖАСИ

М 1:50

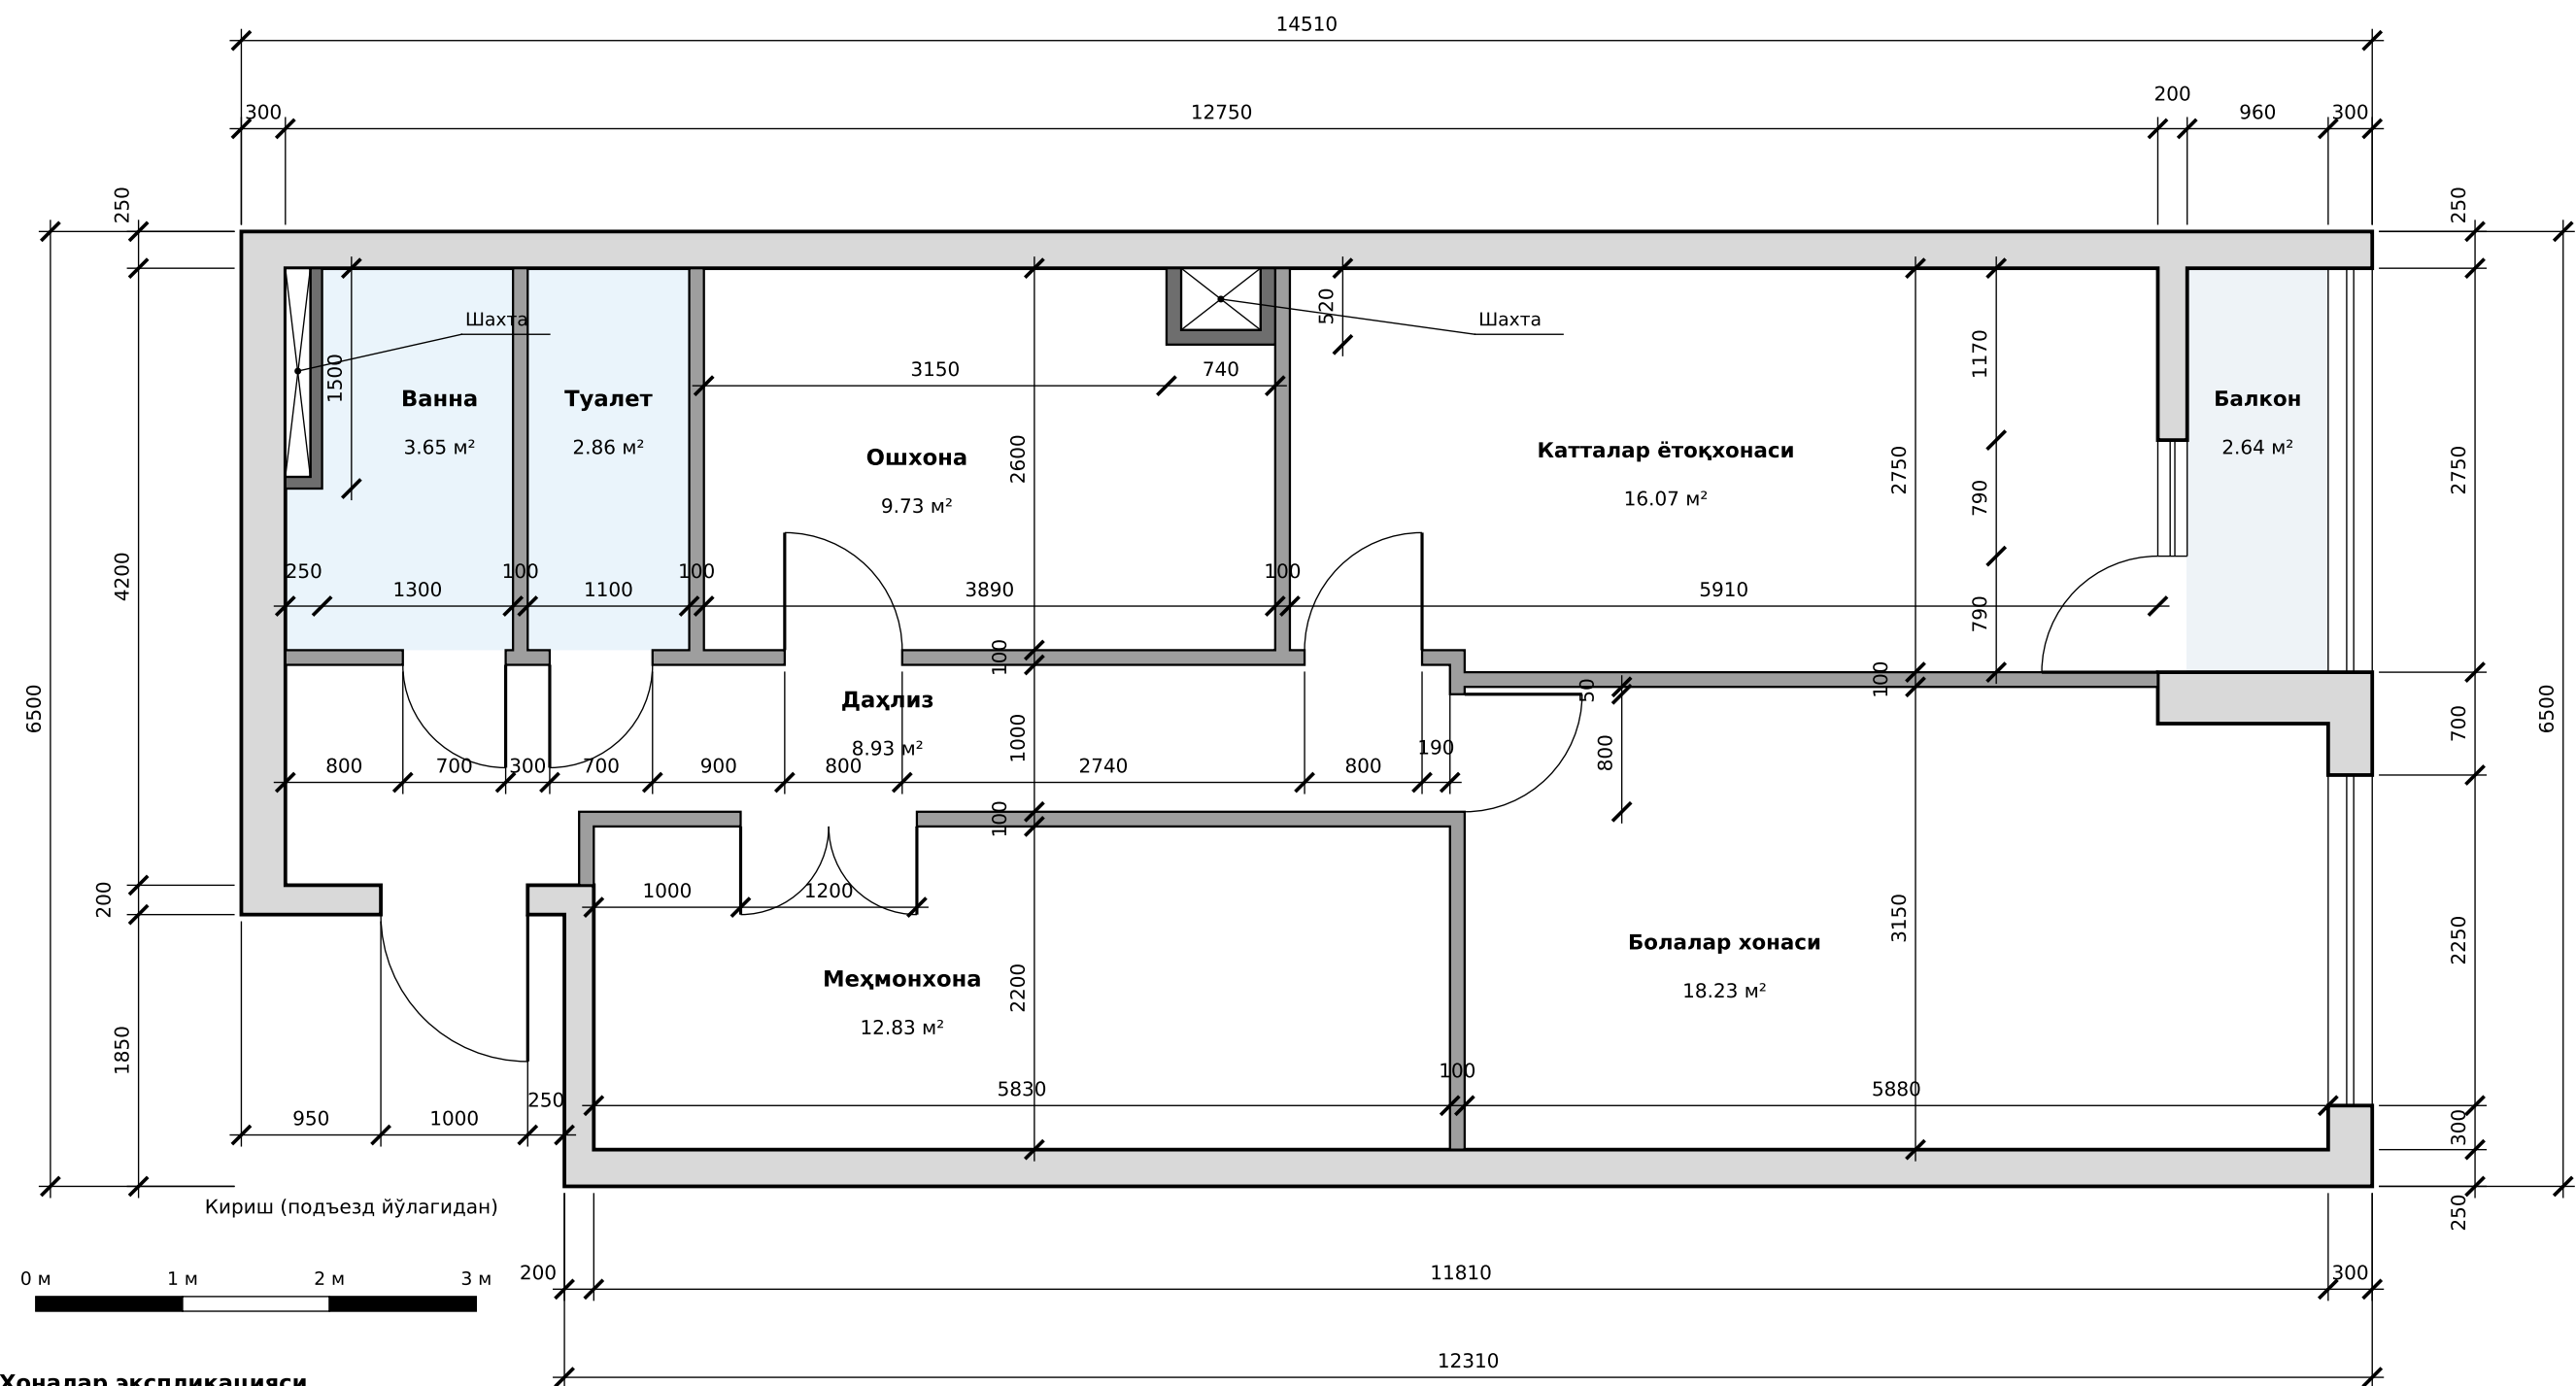

Хоналар экспликацияси

№	Хона номи	Майдон, м²
1	Ванна	3.65
2	Туалет	2.86
3	Ошхона	9.73
4	Катталар ётоқхонаси	16.07
5	Болалар хонаси	18.23
6	Меҳмонхона	12.83
7	Даҳлиз	8.93
	Жами (балконсиз)	72.31
8	Балкон	2.64

- Изоҳлар:
- Барча ўлчамлар миллиметрда.
 - Янги ички деворлар 100 мм, даҳлиз кенглиги 1000 мм.
 - Эшик ўринлари: ванна ва туалет 700 мм, ошхона, ётоқхоналар 800 мм, меҳмонхона 1200 мм икки табақали.
 - Ванна ва туалет эшиклари даҳлизга очилади.
 - Шахталар ўз ўрнида сақланган.
 - Ташқи девор қалинликлари манба расмдан тахминий олинган, жойида текширилсин.

Объект	Квартира (қайта режалаштириш)
Чизма	Хоналар режаси, ички деворлар
Масштаб	1:50
Формат	A3
Сана	24.09.2026