


ДИЗАЙН-ПЛАНИРОВКА / FURNISHED DESIGN LAYOUT

М 1:50

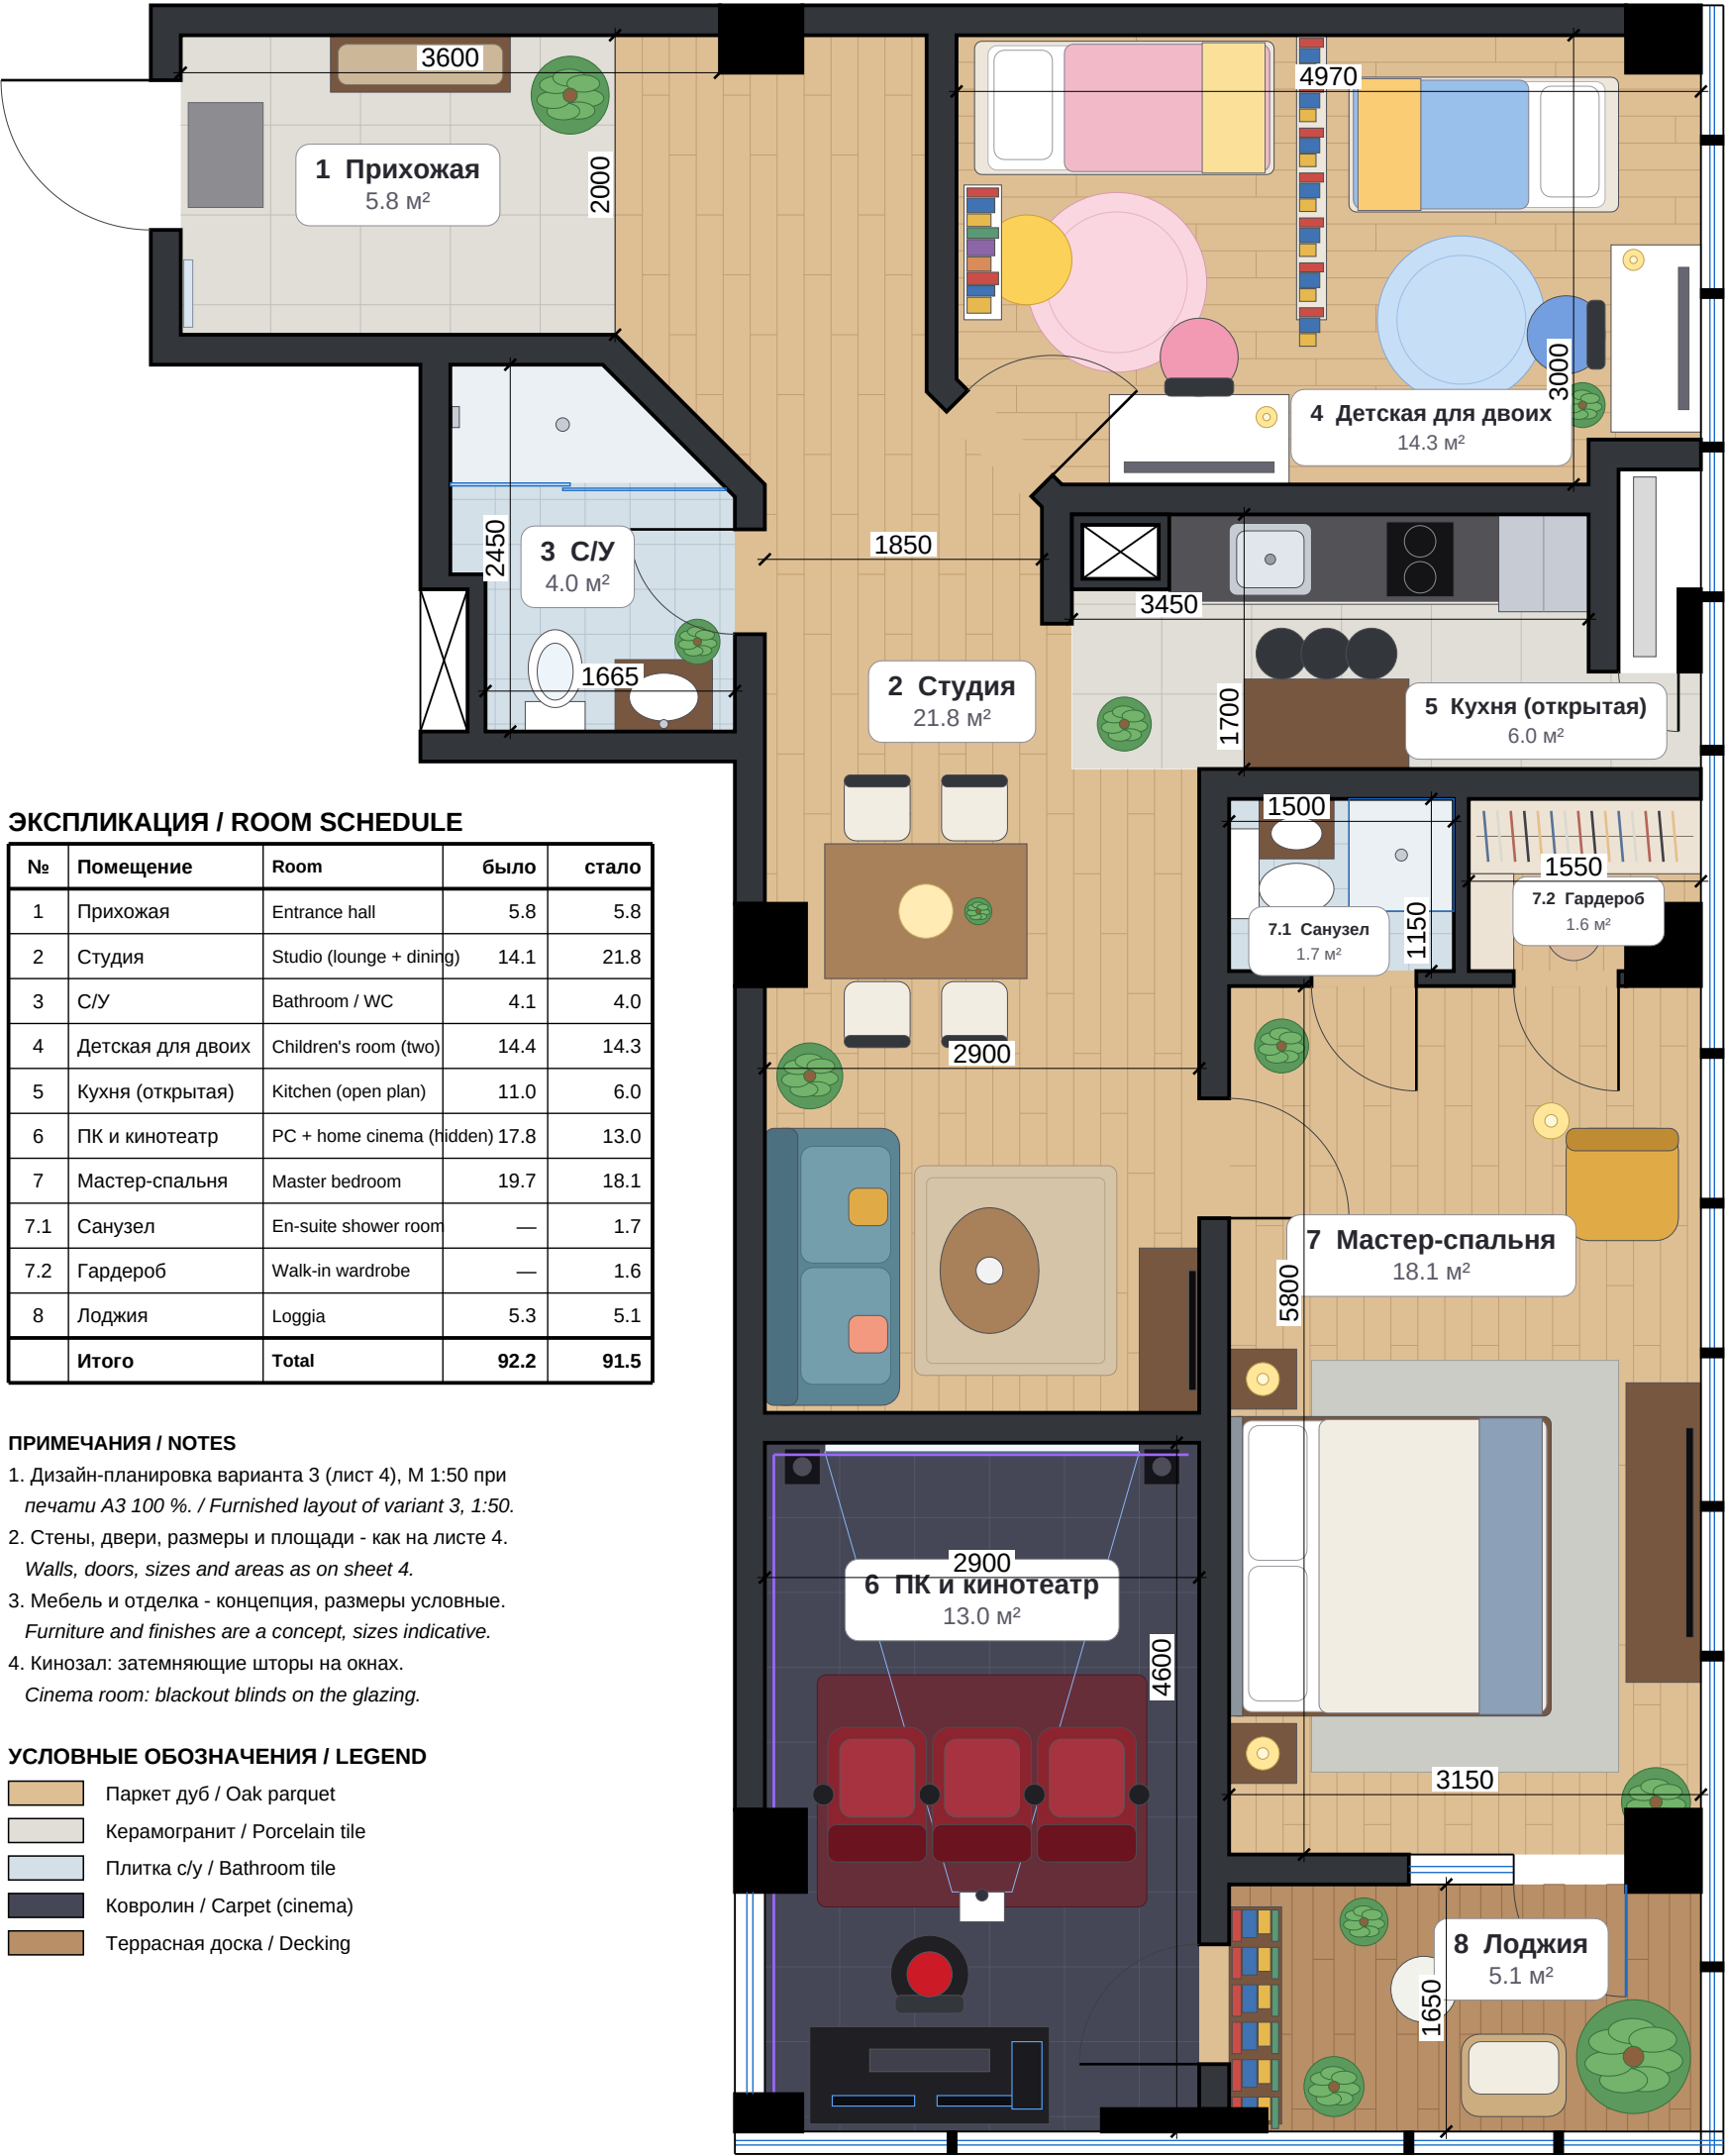

ЭКСПЛИКАЦИЯ / ROOM SCHEDULE

№	Помещение	Room	было	стало
1	Прихожая	Entrance hall	5.8	5.8
2	Студия	Studio (lounge + dining)	14.1	21.8
3	С/У	Bathroom / WC	4.1	4.0
4	Детская для двоих	Children's room (two)	14.4	14.3
5	Кухня (открытая)	Kitchen (open plan)	11.0	6.0
6	ПК и кинотеатр	PC + home cinema (hidden)	17.8	13.0
7	Мастер-спальня	Master bedroom	19.7	18.1
7.1	Санузел	En-suite shower room	—	1.7
7.2	Гардероб	Walk-in wardrobe	—	1.6
8	Лоджия	Loggia	5.3	5.1
Итого		Total	92.2	91.5

ПРИМЕЧАНИЯ / NOTES

1. Дизайн-планировка варианта 3 (лист 4), М 1:50 при печати А3 100 %. / *Furnished layout of variant 3, 1:50.*
2. Стены, двери, размеры и площади - как на листе 4. *Walls, doors, sizes and areas as on sheet 4.*
3. Мебель и отделка - концепция, размеры условные. *Furniture and finishes are a concept, sizes indicative.*
4. Кинозал: затемняющие шторы на окнах. *Cinema room: blackout blinds on the glazing.*

УСЛОВНЫЕ ОБОЗНАЧЕНИЯ / LEGEND

- Паркет дуб / Oak parquet
- Керамогранит / Porcelain tile
- Плитка с/у / Bathroom tile
- Ковролин / Carpet (cinema)
- Террасная доска / Decking

Масштабная линейка / Scale bar 1:50 (м / m)



Дизайн-планировка с мебелью (вариант 3)

Furnished colour design layout (replanning variant 3)

Общая площадь / Total area (по чертежу / measured):
91.5 м² (в т.ч. лоджия / incl. loggia 5.1 м²)

Размеры в мм / Dimensions in mm
Основа / Base: output/flat-plan_1-50_A3.pdf

Масштаб / Scale
1:50

Формат / Size
A3

Лист / Sheet
5

Дата / Date
27.09.2026