


ПЛАН ПЕРЕПЛАНИРОВКИ / REPLANNING PROPOSAL

М 1:50

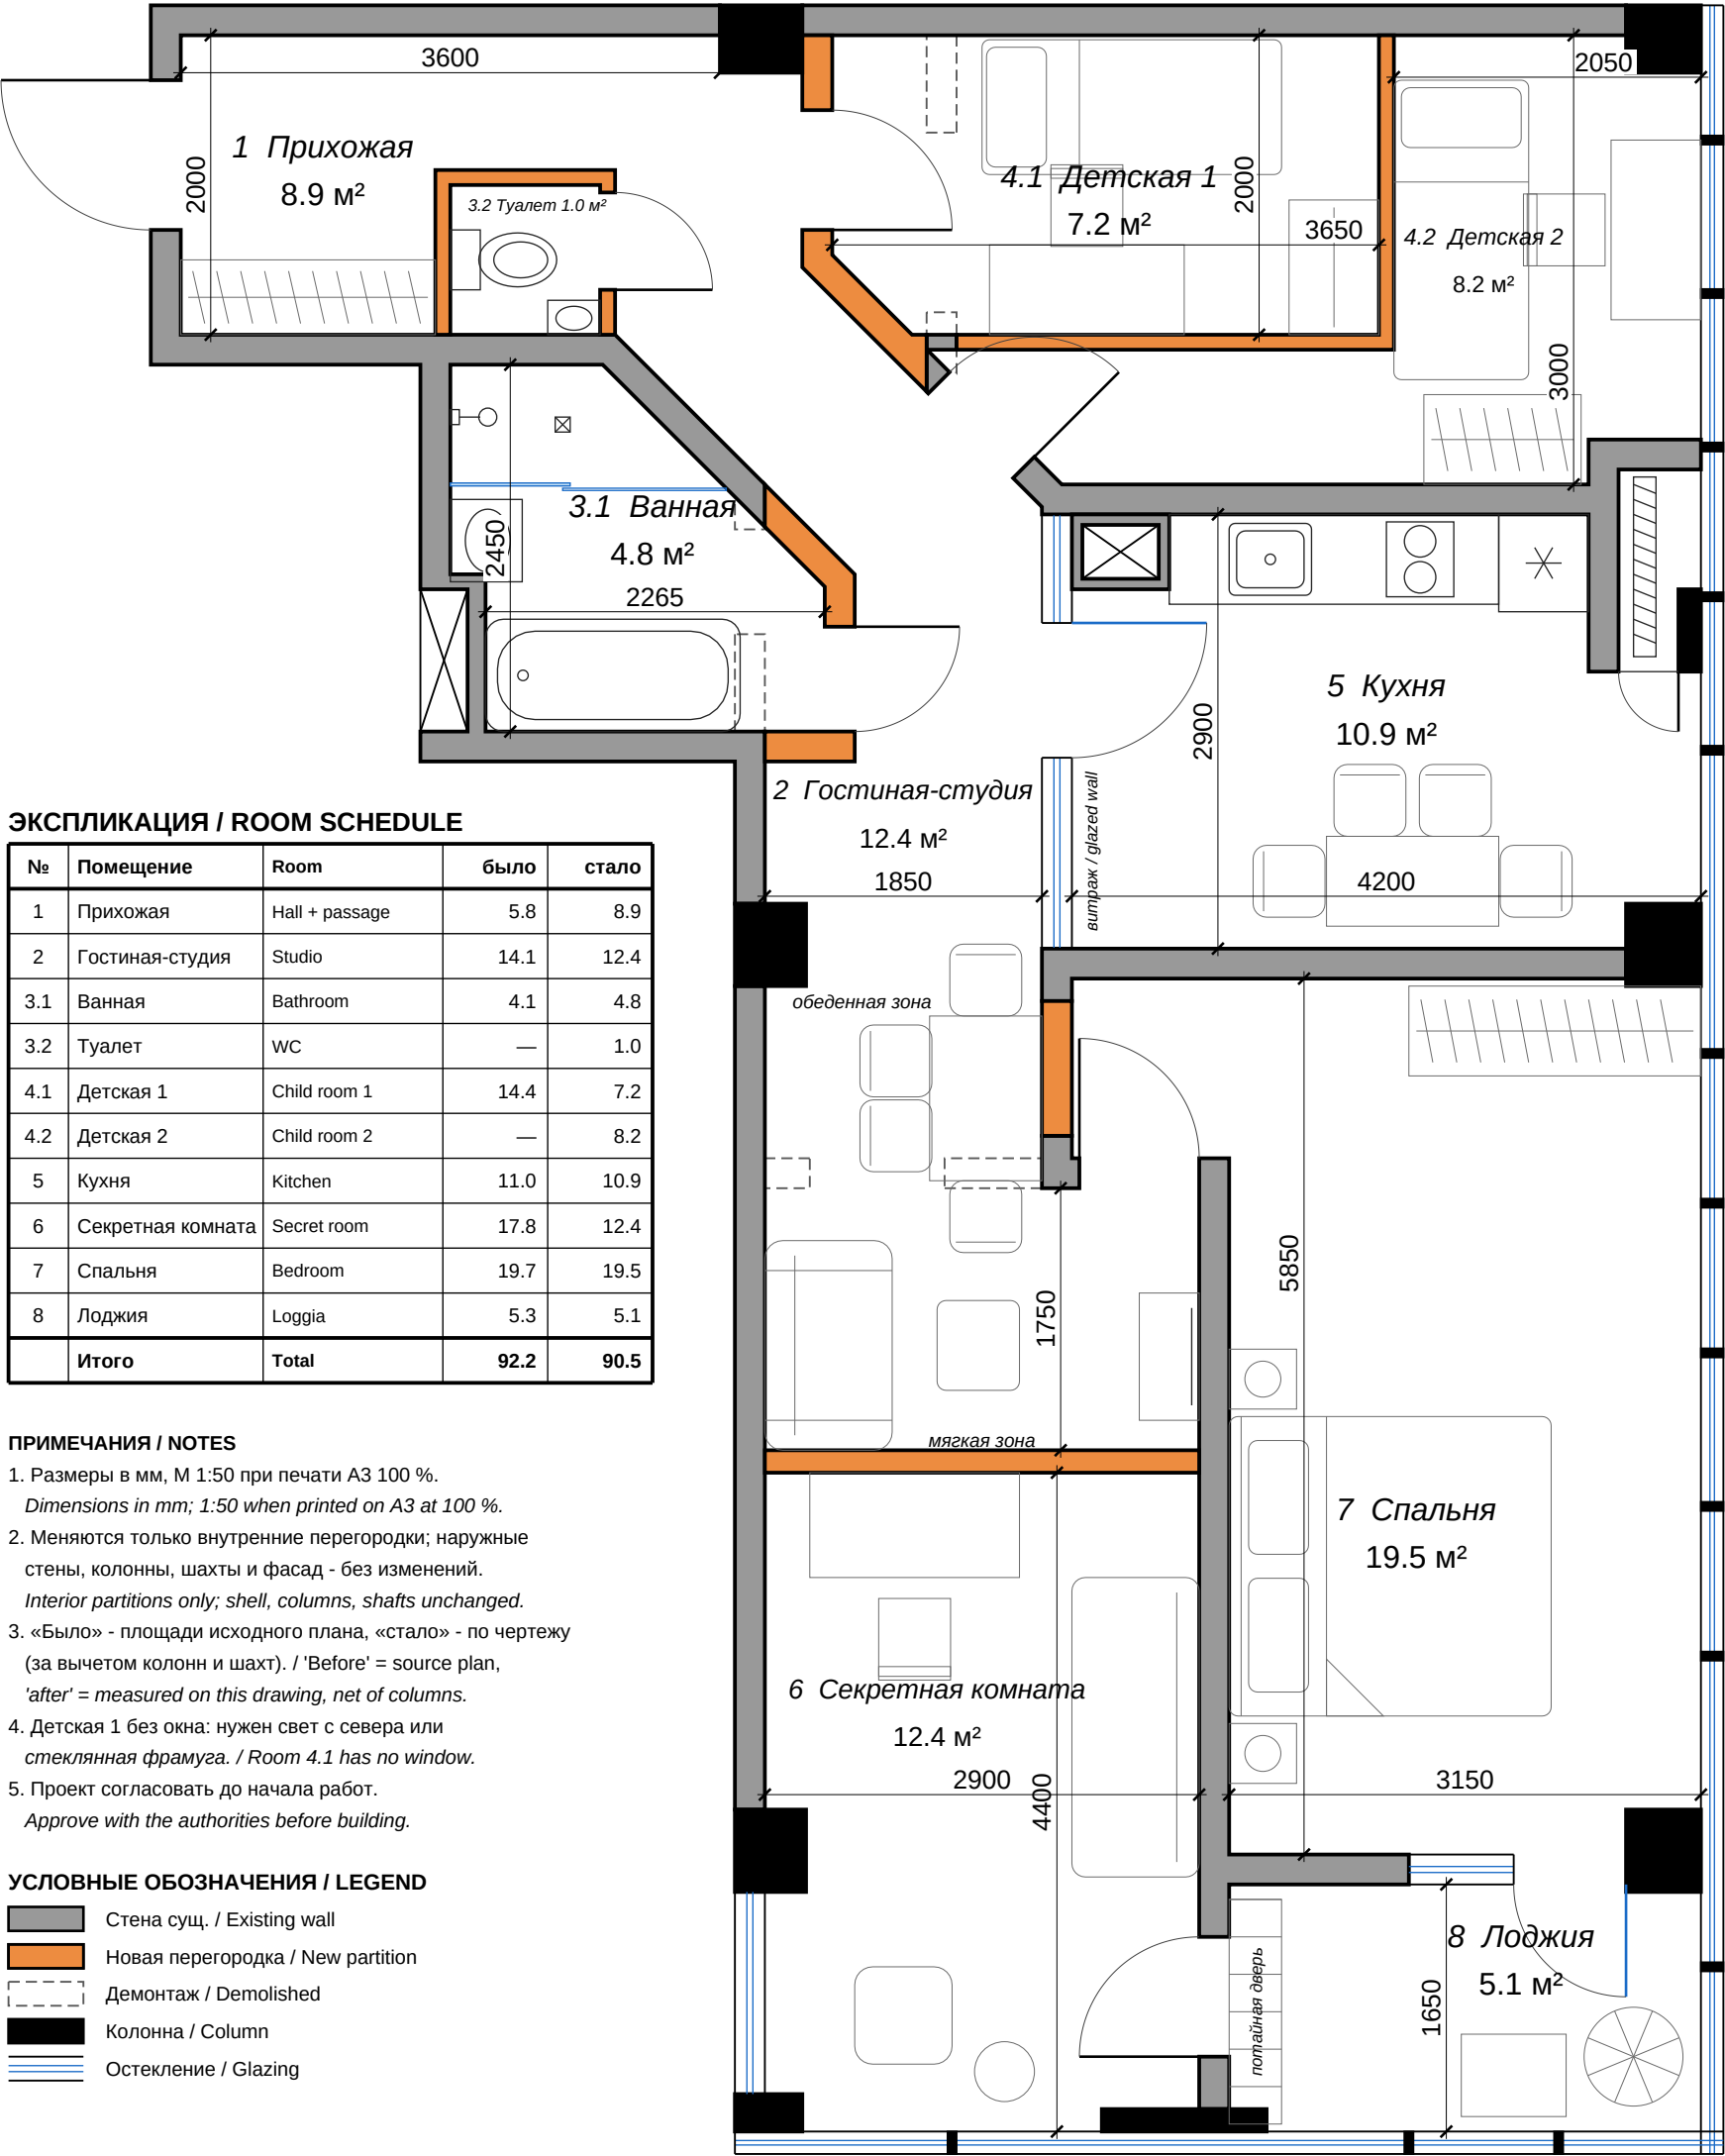

ЭКСПЛИКАЦИЯ / ROOM SCHEDULE

| №     | Помещение         | Room           | было | стало |
|-------|-------------------|----------------|------|-------|
| 1     | Прихожая          | Hall + passage | 5.8  | 8.9   |
| 2     | Гостиная-студия   | Studio         | 14.1 | 12.4  |
| 3.1   | Ванная            | Bathroom       | 4.1  | 4.8   |
| 3.2   | Туалет            | WC             | —    | 1.0   |
| 4.1   | Детская 1         | Child room 1   | 14.4 | 7.2   |
| 4.2   | Детская 2         | Child room 2   | —    | 8.2   |
| 5     | Кухня             | Kitchen        | 11.0 | 10.9  |
| 6     | Секретная комната | Secret room    | 17.8 | 12.4  |
| 7     | Спальня           | Bedroom        | 19.7 | 19.5  |
| 8     | Лоджия            | Loggia         | 5.3  | 5.1   |
| Итого |                   | Total          | 92.2 | 90.5  |

ПРИМЕЧАНИЯ / NOTES

1. Размеры в мм, М 1:50 при печати А3 100 %.  
Dimensions in mm; 1:50 when printed on A3 at 100 %.
2. Меняются только внутренние перегородки; наружные стены, колонны, шахты и фасад - без изменений.  
Interior partitions only; shell, columns, shafts unchanged.
3. «Было» - площади исходного плана, «стало» - по чертежу (за вычетом колонн и шахт). / 'Before' = source plan, 'after' = measured on this drawing, net of columns.
4. Детская 1 без окна: нужен свет с севера или стеклянная фрамуга. / Room 4.1 has no window.
5. Проект согласовать до начала работ.  
Approve with the authorities before building.

УСЛОВНЫЕ ОБОЗНАЧЕНИЯ / LEGEND

- Стена сущ. / Existing wall
- Новая перегородка / New partition
- Демонтаж / Demolished
- Колонна / Column
- Остекление / Glazing

Масштабная линейка / Scale bar 1:50 (м / m)



План квартиры - вариант перепланировки

Apartment floor plan - replanning proposal (interior walls only)

Общая площадь / Total area (по чертежу / measured):  
90.5 м² (в т.ч. лоджия / incl. loggia 5.1 м²)

Размеры в мм / Dimensions in mm  
Основа / Base: output/flat-plan\_1-50\_A3.pdf

Масштаб / Scale  
1:50

Формат / Size  
A3

Лист / Sheet  
2

Дата / Date  
27.09.2026