


МЕБЕЛЛАР ЖОЙЛАШУВИ РЕЖАСИ

М 1:50

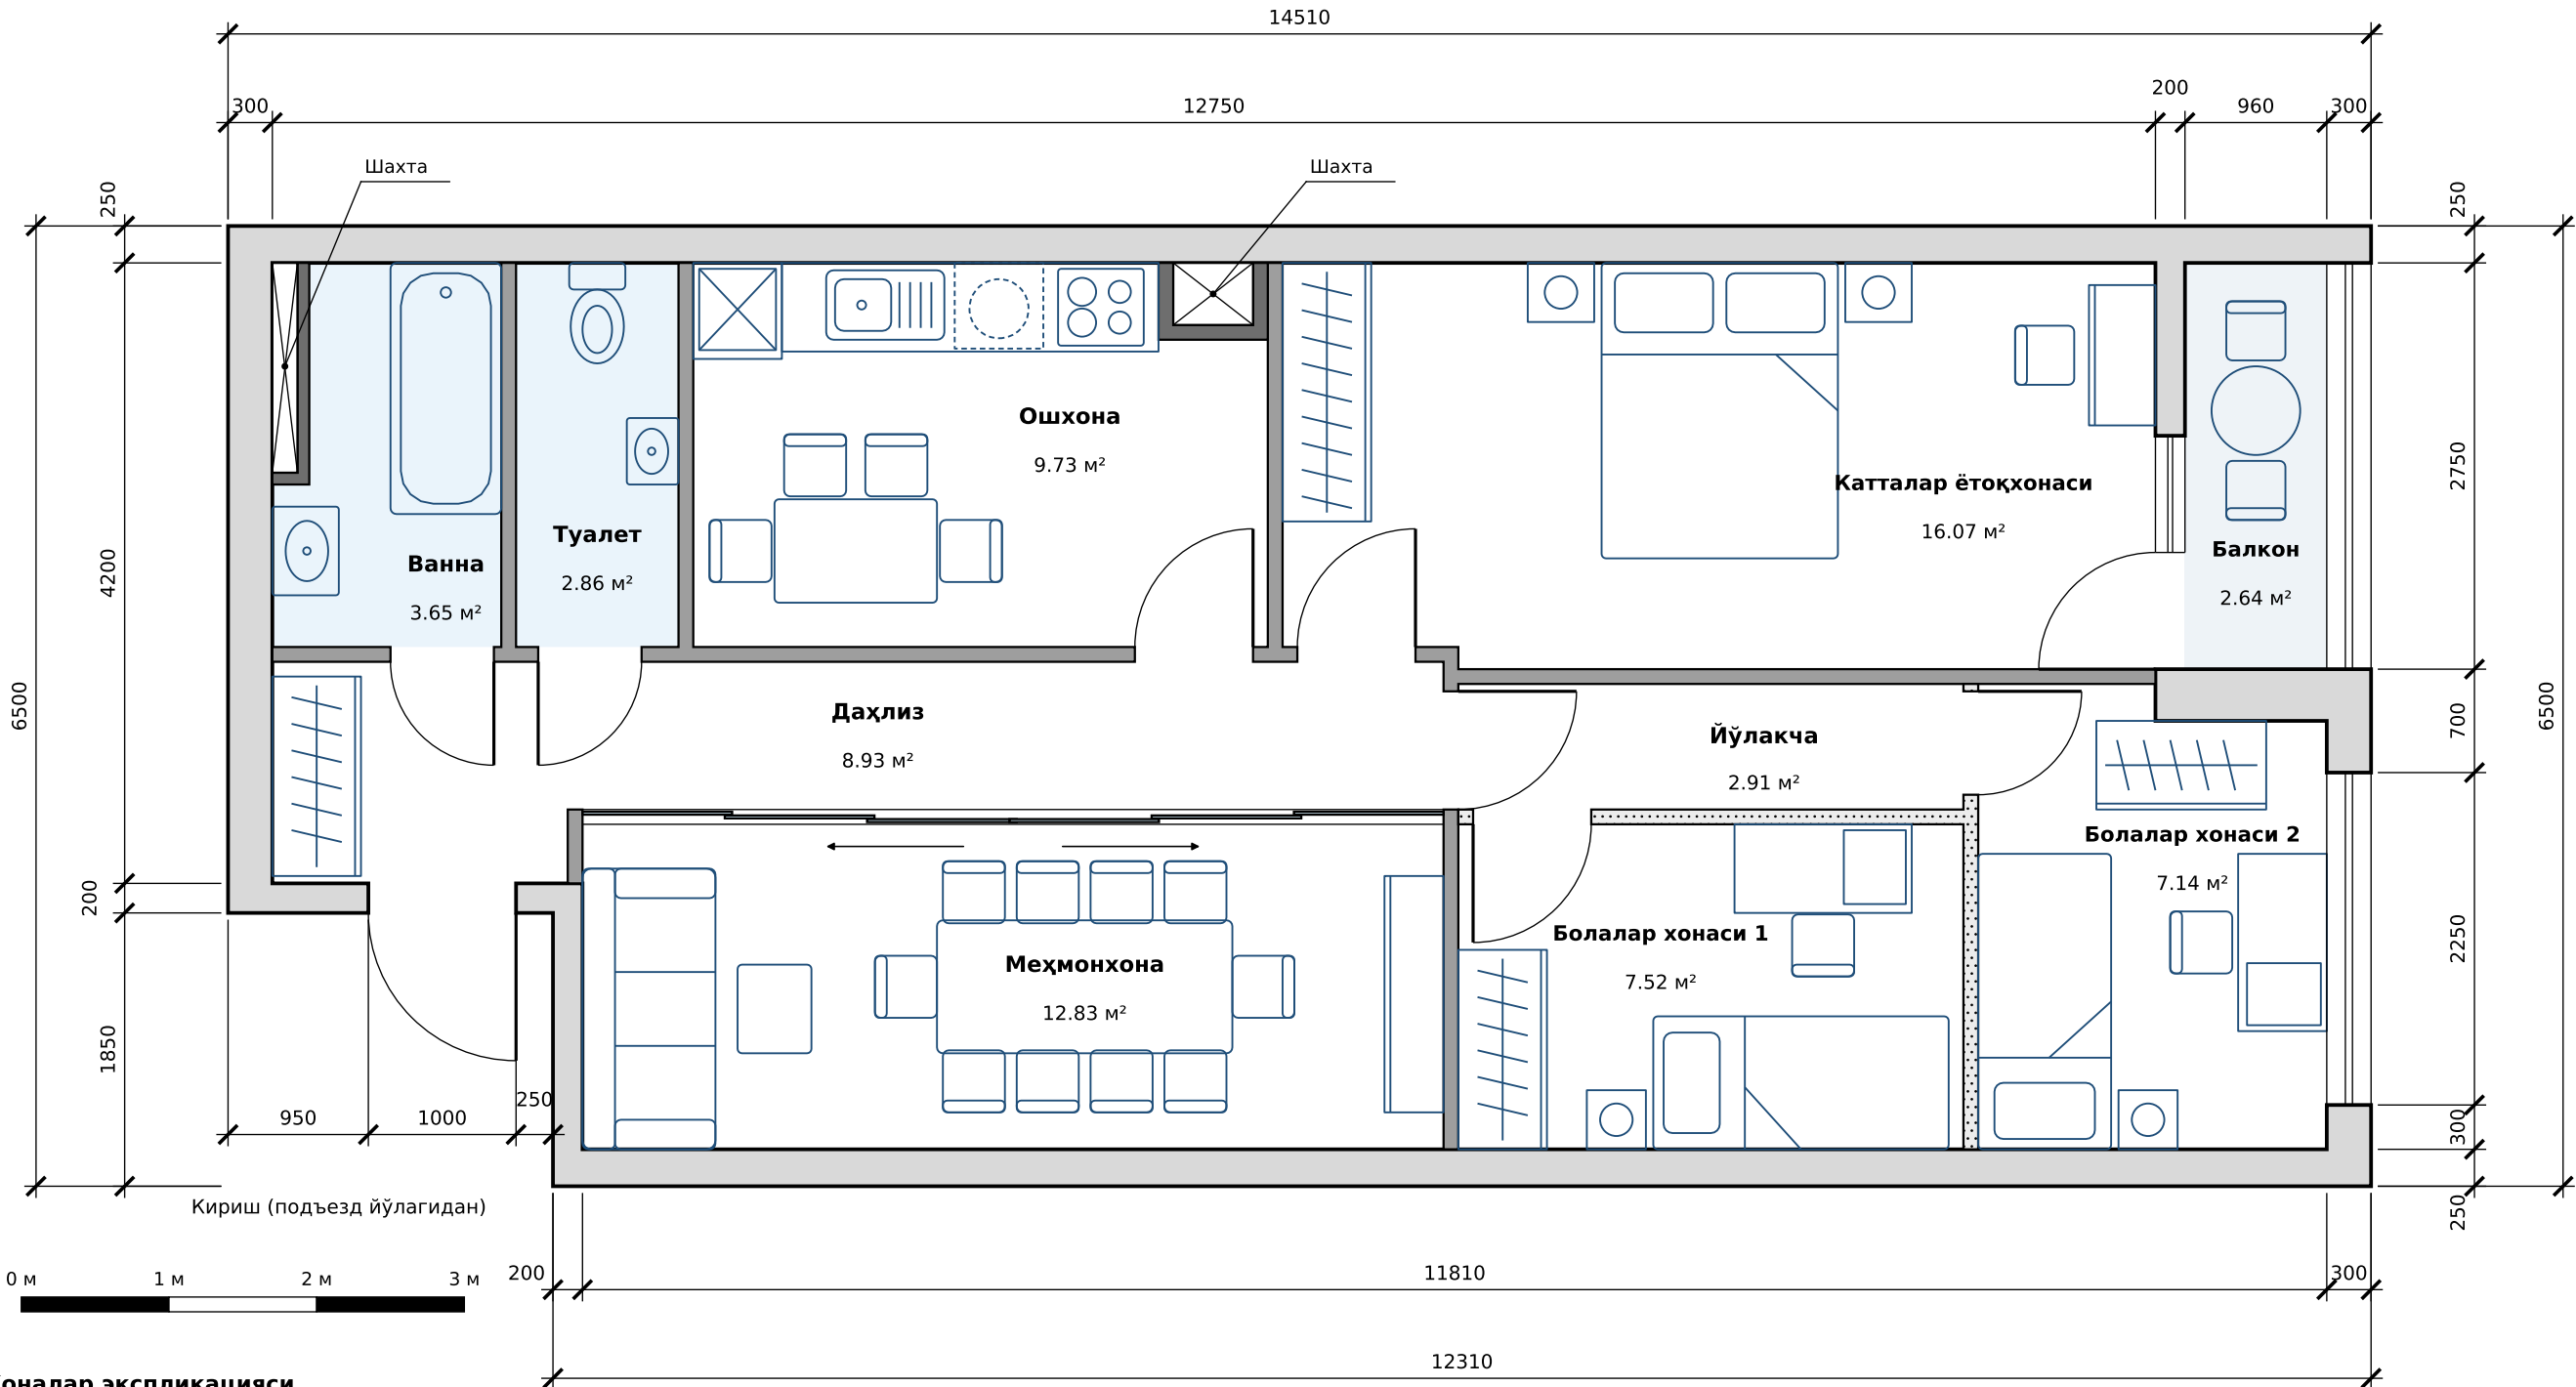

Хоналар экспликацияси

№	Хона номи	Майдон, м²
1	Ванна	3.65
2	Туалет	2.86
3	Ошхона	9.73
4	Катталар ётоқхонаси	16.07
5	Болалар хонаси 1	7.52
6	Болалар хонаси 2	7.14
7	Йўлакча	2.91
8	Меҳмонхона	12.83
9	Даҳлиз	8.93
	Жами (балконсиз)	71.65
10	Балкон	2.64

- Изоҳлар:
- Барча ўлчамлар миллиметрда.
 - Мебеллар стандарт ўлчамларда: катта каравот 1600×2000, болалар каравоти 900×2000, шкафлар 600 чуқурликда, ошхона ишчи юзаси 600.
 - Штрих чизиқ: кир ювиш машинаси ишчи юза остида.
 - Ошхона эшиги стол сиғиши учун ўнг четга кўчирилди.
 - Эшиклар очилиш зонаси мебелдан бўш қолдирилган.

Объект	Квартира (қайта режалаштириш)
Чизма	Мебеллар жойлашуви
Масштаб	1:50
Формат	A3
Сана	24.09.2026