


ПЕРЕПЛАНИРОВКА, ВАРИАНТ 3 / REPLANNING, VARIANT 3

М 1:50

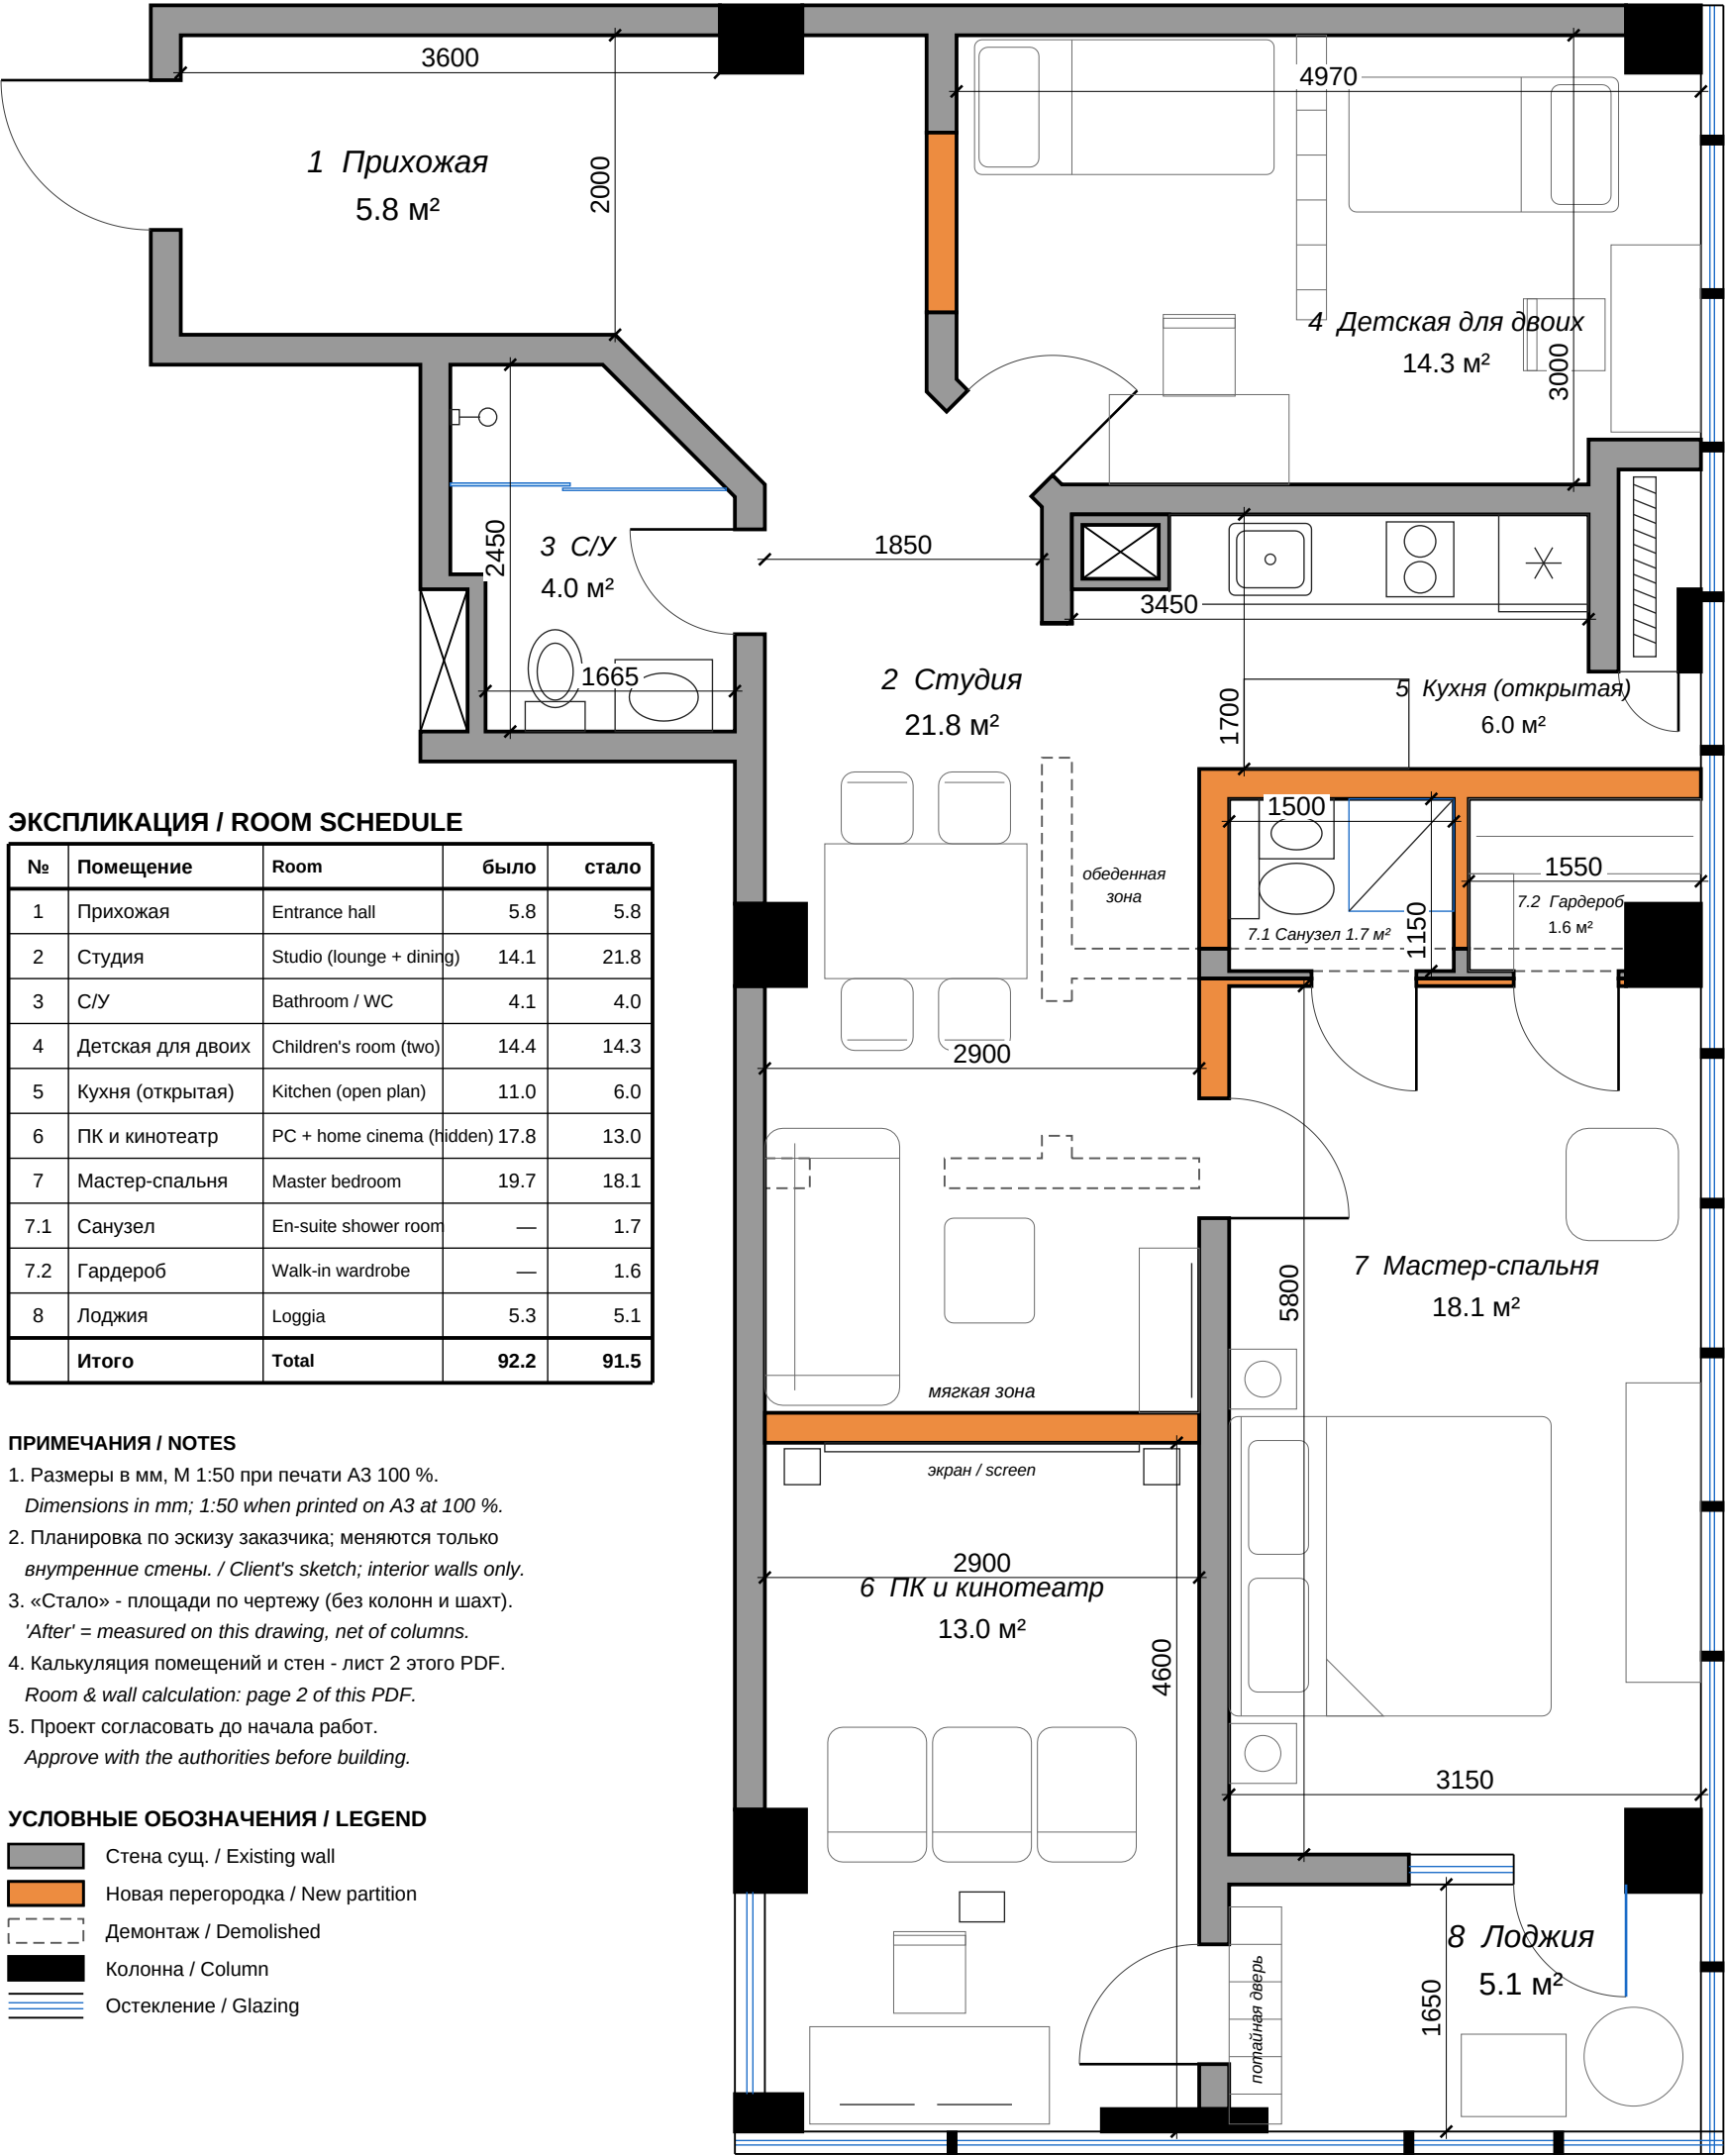

ЭКСПЛИКАЦИЯ / ROOM SCHEDULE

№	Помещение	Room	было	стало
1	Прихожая	Entrance hall	5.8	5.8
2	Студия	Studio (lounge + dining)	14.1	21.8
3	С/У	Bathroom / WC	4.1	4.0
4	Детская для двоих	Children's room (two)	14.4	14.3
5	Кухня (открытая)	Kitchen (open plan)	11.0	6.0
6	ПК и кинотеатр	PC + home cinema (hidden)	17.8	13.0
7	Мастер-спальня	Master bedroom	19.7	18.1
7.1	Санузел	En-suite shower room	—	1.7
7.2	Гардероб	Walk-in wardrobe	—	1.6
8	Лоджия	Loggia	5.3	5.1
Итого		Total	92.2	91.5

ПРИМЕЧАНИЯ / NOTES

- Размеры в мм, М 1:50 при печати А3 100 %.
Dimensions in mm; 1:50 when printed on A3 at 100 %.
- Планировка по эскизу заказчика; меняются только внутренние стены. / Client's sketch; interior walls only.
- «Стало» - площади по чертежу (без колонн и шахт).
'After' = measured on this drawing, net of columns.
- Калькуляция помещений и стен - лист 2 этого PDF.
Room & wall calculation: page 2 of this PDF.
- Проект согласовать до начала работ.
Approve with the authorities before building.

УСЛОВНЫЕ ОБОЗНАЧЕНИЯ / LEGEND

- Стена сущ. / Existing wall
- Новая перегородка / New partition
- Демонтаж / Demolished
- Колонна / Column
- Остекление / Glazing

Масштабная линейка / Scale bar 1:50 (м / m)



План квартиры - перепланировка, вариант 3

Apartment floor plan - replanning variant 3 (client's sketch)

Общая площадь / Total area (по чертежу / measured):
91.5 м² (в т.ч. лоджия / incl. loggia 5.1 м²)

Размеры в мм / Dimensions in mm
Основа / Base: output/flat-plan_1-50_A3.pdf

Масштаб / Scale
1:50

Формат / Size
A3

Лист / Sheet
4

Дата / Date
27.09.2026

КАЛЬКУЛЯЦИЯ ПОМЕЩЕНИЙ И СТЕН / ROOMS & WALLS CALCULATION

Вариант 3 (по эскизу заказчика), лист 4 - все размеры сняты с плана М 1:50, мм

1. Помещения / Rooms

№	Помещение	Room	Габарит, мм	S, м²	P, м	Было, м²
1	Прихожая	Entrance hall	2900 × 2000	5.80	9.80	5.8
2	Студия	Studio (lounge + dining)	3900 × 9200	21.80	26.21	14.1
3	С/У	Bathroom / WC	1900 × 2450	4.02	8.18	4.1
4	Детская для двоих	Children's room (two)	4970 × 3000	14.31	15.53	14.4
5	Кухня (открытая)	Kitchen (open plan)	4200 × 1700	6.02	11.82	11.0
6	ПК и кинотеатр	PC + home cinema (hidden)	2900 × 4600	13.03	15.55	17.8
7	Мастер-спальня	Master bedroom	3150 × 5800	18.12	17.90	19.7
7.1	Санузел	En-suite shower room	1500 × 1150	1.73	5.30	—
7.2	Гардероб	Walk-in wardrobe	1550 × 1150	1.56	5.40	—
8	Лоджия	Loggia	3150 × 1650	5.13	9.60	5.3
Итого / Total				91.52		92.2

Габарит - наибольшие размеры помещения в свету; S - площадь пола по чертежу (без колонн, шахт, стен); P - периметр пола (для плинтуса).
Width x length = clear overall size; S = floor area on this drawing (net of columns, shafts, walls); P = floor perimeter (skirting).

2. Новые стены и перегородки / New walls & partitions

№	Элемент / Element	Длина, мм	Толщ., мм	S сеч., м²	п.м
1	Заделка двери гостиной / infill of old living-room door	1200	200	0.240	1.20
2	Южная стена кухни / kitchen south wall	3350	200	0.670	3.35
3	Западная стена спальни (новые участки) / master-bedroom west wall (new parts)	1800	200	0.360	1.80
4	Санузел гардероб / en-suite wardrobe	1150	100	0.115	1.15
5	Санузел, гардероб спальня (без 2 дверей) / en-suite + wardrobe bedroom (less 2 doors)	1250	100	0.125	1.25
6	Студия секретная комната / studio secret room	2900	200	0.580	2.90
Итого / Total				2.090	11.65

Площадь стены под отделку/кладку = длина × высота потолка (с каждой стороны). Wall face area = length × ceiling height (per side).

3. Демонтаж / Demolition

№	Элемент / Element	Длина, мм	Толщ., мм	S сеч., м²	п.м
1	Западная стена кухни (ниже проёма) / kitchen west wall below the door	1625	200	0.325	1.62
2	Кухня спальня 7, западная часть / kitchen bedroom 7, west part	850	200	0.170	0.85
3	Кухня спальня 7, восточная часть / kitchen bedroom 7, east part	2650	200	0.530	2.65
4	Откос бывшей двери спальни 7 / jamb of old bedroom-7 door	150	200	0.030	0.15
5	Коридор спальня 6 / corridor bedroom 6	2000	200	0.400	2.00
6	Проём в стене у новой двери спальни / cut for new bedroom door	400	200	0.080	0.40
7	Проём в 45° стене детской / cut for children's-room door	800	200	0.160	0.80
Итого / Total				1.695	8.47

4. Новые дверные проёмы / New door openings (ширина в свету / clear width, мм)

№	Проём	Opening	Ширина
1	Детская (в 45° стене)	Children's room (45° wall)	800
2	Мастер-спальня (из студии)	Master bedroom (from studio)	800
3	Санузел при спальне	En-suite	700
4	Гардероб	Walk-in wardrobe	700
5	Потайная дверь-стеллаж (из лоджии)	Hidden bookcase door (from loggia)	800

Стены сняты с эскиза заказчика (1 рх эскиза = 10,5 мм) и округлены до 50 мм; толщина новых стен 200/100 мм.
Walls read from the client's sketch (1 sketch px = 10.5 mm) and rounded to 50 mm; new walls 200 / 100 mm.
Санузел 7.1 далеко от стояков - нужен трап/насос и согласование. / En-suite is far from the risers: pump + approval.
Перепланировку согласовать до начала работ. / Approve the replanning with the authorities before building.