


КВАРТИРАНИ ҚАЙТА РЕЖАЛАШТИРИШ РЕЖАСИ

М 1:50

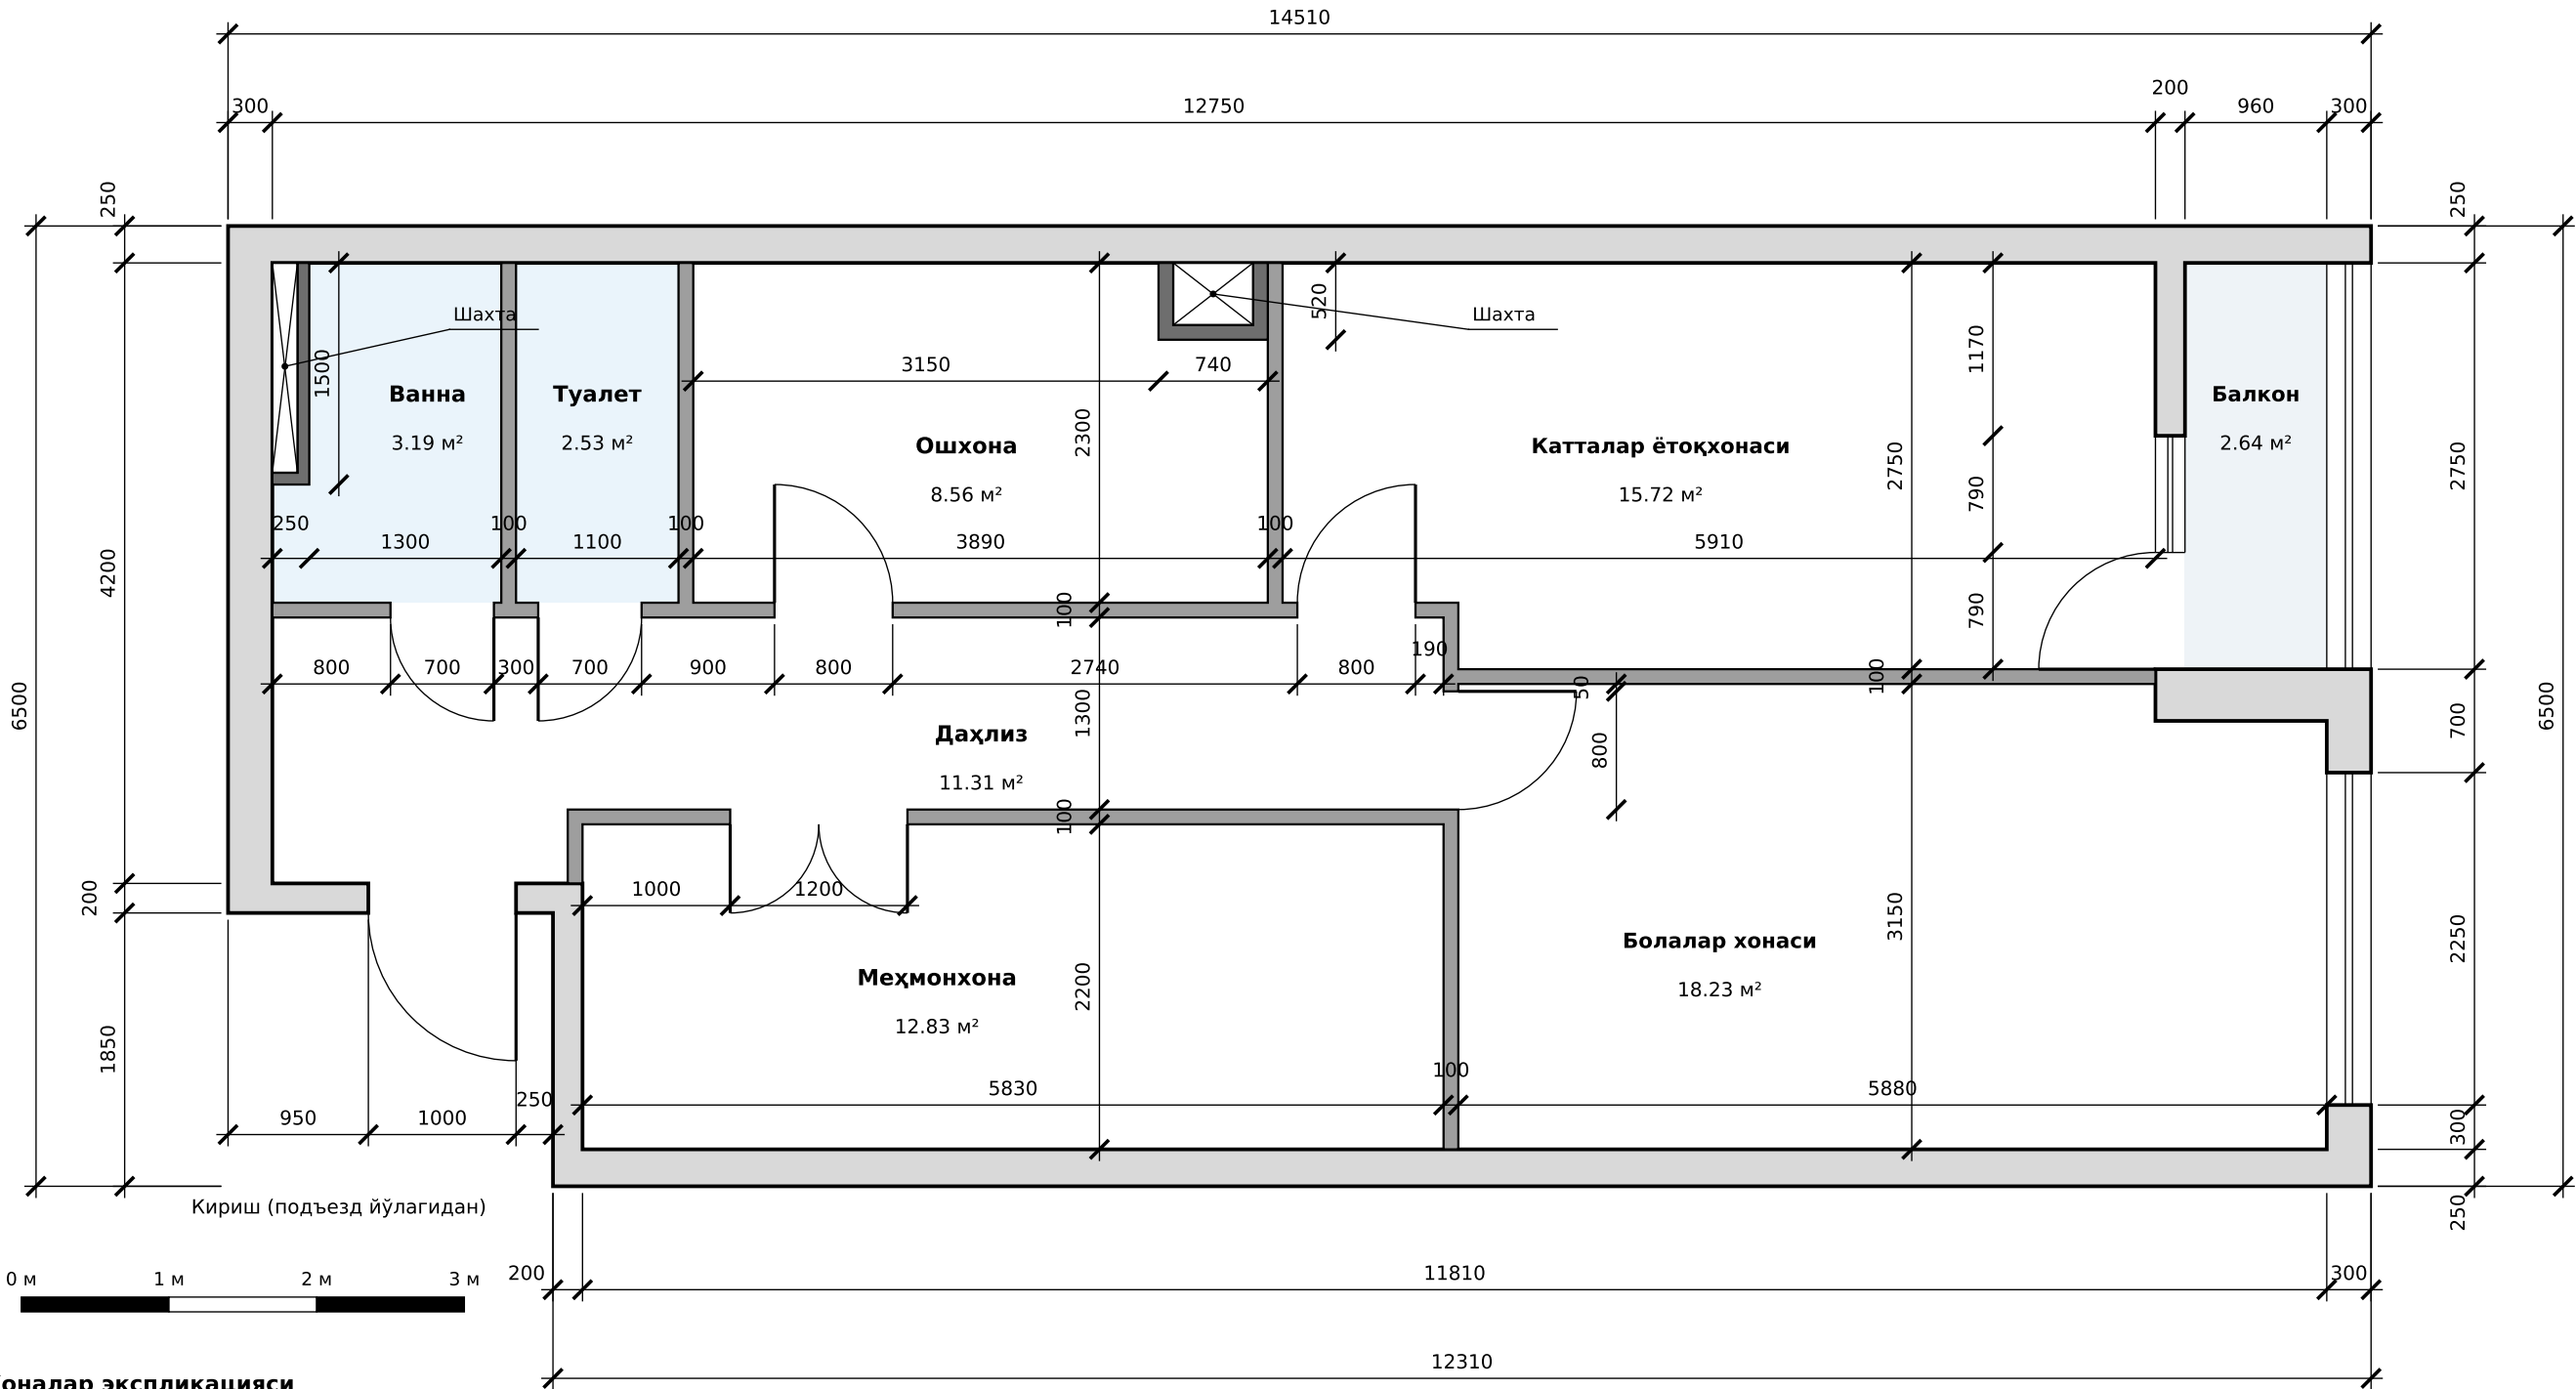

Хоналар экспликацияси

№	Хона номи	Майдон, м²
1	Ванна	3.19
2	Туалет	2.53
3	Ошхона	8.56
4	Катталар ётоқхонаси	15.72
5	Болалар хонаси	18.23
6	Меҳмонхона	12.83
7	Даҳлиз	11.31
	Жами (балконсиз)	72.37
8	Балкон	2.64

- Изоҳлар:
- Барча ўлчамлар миллиметрда.
 - Янги ички деворлар 100 мм қалинликда.
 - Эшик ўринлари: ванна ва туалет 700 мм, ошхона, ётоқхоналар 800 мм, меҳмонхона 1200 мм икки табақали.
 - Ванна ва туалет эшиклари даҳлизга очилади.
 - Шахталар ўз ўрнида сақланган.
 - Ташқи девор қалинликлари манба расмдан тахминий олинган, жойида текширилсин.

Объект	Квартира (қайта режалаштириш)
Чизма	Хоналар режаси, ички деворлар
Масштаб	1:50
Формат	A3
Сана	24.09.2026